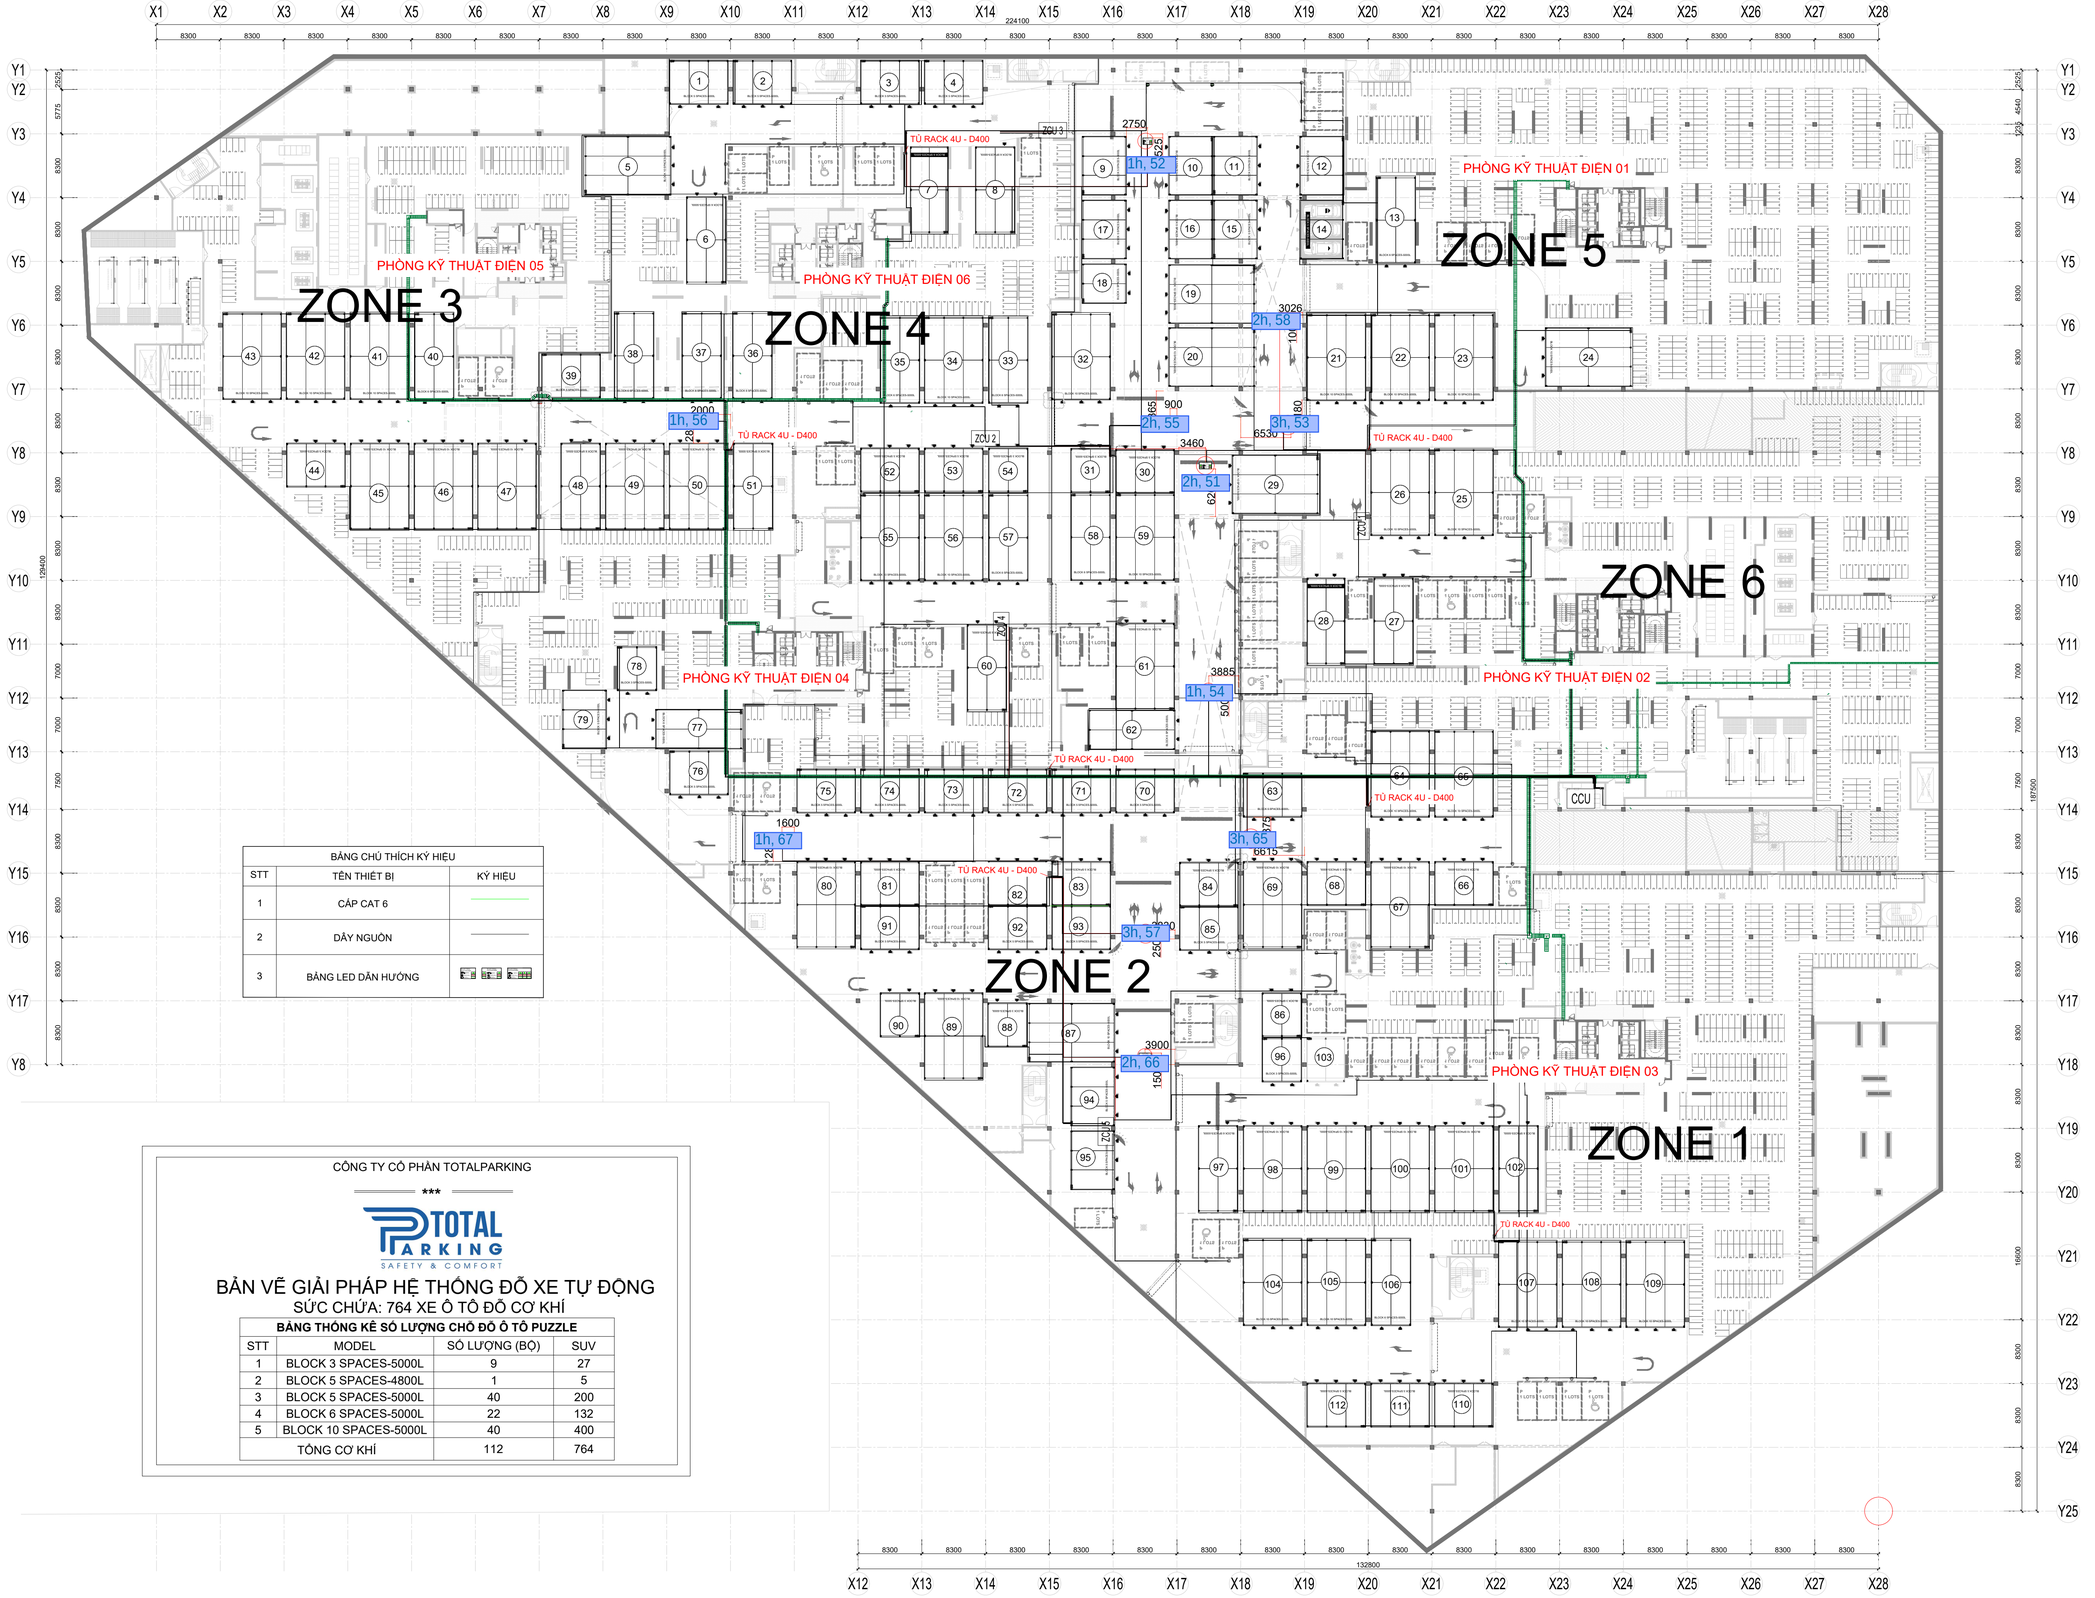


BẢNG CHÚ THÍCH KÝ HIỆU

STT	TÊN THIẾT BỊ	KÝ HIỆU
1	CÁP CAT 6	
2	DÂY NGUỒN	
3	BẢNG LED DẪN HƯỚNG	

CÔNG TY CỔ PHẦN TOTALPARKING

BẢN VẼ GIẢI PHÁP HỆ THỐNG ĐỖ XE TỰ ĐỘNG

SỨC CHỨA: 764 XE Ô TÔ ĐỖ CƠ KHÍ

BẢNG THỐNG KÊ SỐ LƯỢNG CHỖ ĐỖ Ô TÔ PUZZLE

STT	MODEL	SỐ LƯỢNG (BỘ)	SUV
1	BLOCK 3 SPACES-5000L	9	27
2	BLOCK 5 SPACES-4800L	1	5
3	BLOCK 5 SPACES-5000L	40	200
4	BLOCK 6 SPACES-5000L	22	132
5	BLOCK 10 SPACES-5000L	40	400
	TỔNG CƠ KHÍ	112	764

MẶT BẰNG TỔNG THỂ DÂY TÍN HIỆU TẦNG HẦM - CLUSTER 01

PROJECT NAME - TÊN DỰ ÁN:

THE CONSTRUCTION AT LOTS C3-CH01, C3-CH02, C3-CH03, C3-CX01 AND C3-CX02 WITHIN THE NEW URBAN AREA PROJECT OF TAY MO - DAI MO (LUMI HANOI)

CÔNG TRÌNH TẠI LÔ ĐẤT C3-CH01, C3-CH02, C3-CH03, C3-CX01 VÀ C3-CX02 THUỘC DỰ ÁN KHU ĐÔ THỊ MỚI TÂY MỖ - ĐẠI MỖ (LUMI HÀ NỘI)

VENUE - ĐỊA ĐIỂM:
LOT C3-CH01-1, TAY MO - DAI MO NEW URBAN AREA PROJECT - VINHOMES PARK, TAY MO WARD, HANOI CITY.
Ô C3-CH01-1, DỰ ÁN KHU ĐÔ THỊ MỚI TÂY MỖ, ĐẠI MỖ, VINHOMES PARK, PHƯỜNG TÂY MỖ, THÀNH PHỐ HÀ NỘI.

INVESTOR - CHỦ ĐẦU TƯ:

ANH SAO COMMERCIAL DEVELOPMENT AND TRADING LIMITED LIABILITY COMPANY

CÔNG TY TNHH THƯƠNG MẠI VÀ PHÁT TRIỂN KINH DOANH ẢNH SAO

ADDRESS - ĐỊA CHỈ:
LOT C3-CH01-1, TAY MO - DAI MO NEW URBAN AREA PROJECT - VINHOMES PARK, TAY MO WARD, HANOI CITY.
Ô C3-CH01-1, DỰ ÁN KHU ĐÔ THỊ MỚI TÂY MỖ, ĐẠI MỖ, VINHOMES PARK, PHƯỜNG TÂY MỖ, THÀNH PHỐ HÀ NỘI.

TEL: 088480715 FAX: 088465274

Examined with no objection .	Examined, observation added Resubmission not required.	Examined and Resubmission required.
☐	☐	☐

Signature:

Name: Date:

DESIGN CONSULTANT- TƯ VẤN THIẾT KẾ:

CÔNG TY CỔ PHẦN INNO

CREATIVITY AT WORK

INNO.JSC COMPANY

ADDRESS: NO. 87 YEN HOA, YEN HOA, CAU GIAY, HANOI
ĐỊA CHỈ: SỐ 87 YÊN HOA, PH. YÊN HÒA, CẦU GIẤY, HÀ NỘI
TEL: 0243 212 1778 FAX: 0243 212 1778

Examined with no objection .	Examined, observation added Resubmission not required.	Examined and Resubmission required.
☐	☐	☐

Approved by:

Name: Date:

Checked by:

Name: Date:

MAIN CONTRACTOR- NHÀ THẦU THI CÔNG

NEWTECONS INVESTMENT CONSTRUCTION JOINT STOCK COMPANY
CÔNG TY CỔ PHẦN ĐẦU TƯ XÂY DỰNG NEWTECONS

NEWTECONS GROUP

ADDRESS - ĐỊA CHỈ:
NEWTECONS TOWER - 96 PHAN DANG LUU STREET, DUC NHUAN WARD, HO CHI MINH
NEWTECONS TOWER, 96 PHAN ĐĂNG LƯU, PHƯỜNG ĐỨC NHUẬN, THÀNH PHỐ HỒ CHÍ MINH

Approved by:

Name: LƯU VĨNH KIỆT Date:

CONTRACTOR- NHÀ THẦU THI CÔNG

CÔNG TY CỔ PHẦN TOTAL PARKING
TOTAL PARKING
JOINT STOCK COMPANY

TOTAL PARKING SAFETY & COMFORT

ADDRESS - ĐỊA CHỈ:
TÒA NHÀ HAWEE, LÔ D2, KHU ĐẤU GIÁ QSĐ PHƯỜNG HÀ ĐÔNG, TP. HÀ NỘI
LOT D2, LAND USE RIGHT AUTION, HA DONG WARD, HA NOI CITY
TEL: (84) (024) 33 11 7744 / FAX: (84) (024) 33 11 7748

Approved by:

Name: PHẠM MINH CHIẾN Date:

Drawing by:

Name: LÊ TRUNG VỊNH Date:

PACKAGE- GÓI THẦU:

MECHANICAL CAR PARKING SYSTEM

DRAWING TYPE - LOẠI BẢN VẼ:

☐ Method Statement (MOS) ☑ Shop Drawing (SD)

DRAWING NAME - TÊN BẢN VẼ:

MẶT BẰNG TỔNG THỂ DÂY TÍN HIỆU TẦNG HẦM - CLUSTER 01

SUBMIT NO - MÃ BẢN VẼ:	LM-CL1-BAS-NTC-CP-SHD-0003-01.1
REV - PHIÊN BẢN:	01
SCALE - TỈ LỆ:	As indicated
DATE - NGÀY:	
DWG NO - S/H BẢN VẼ:	