


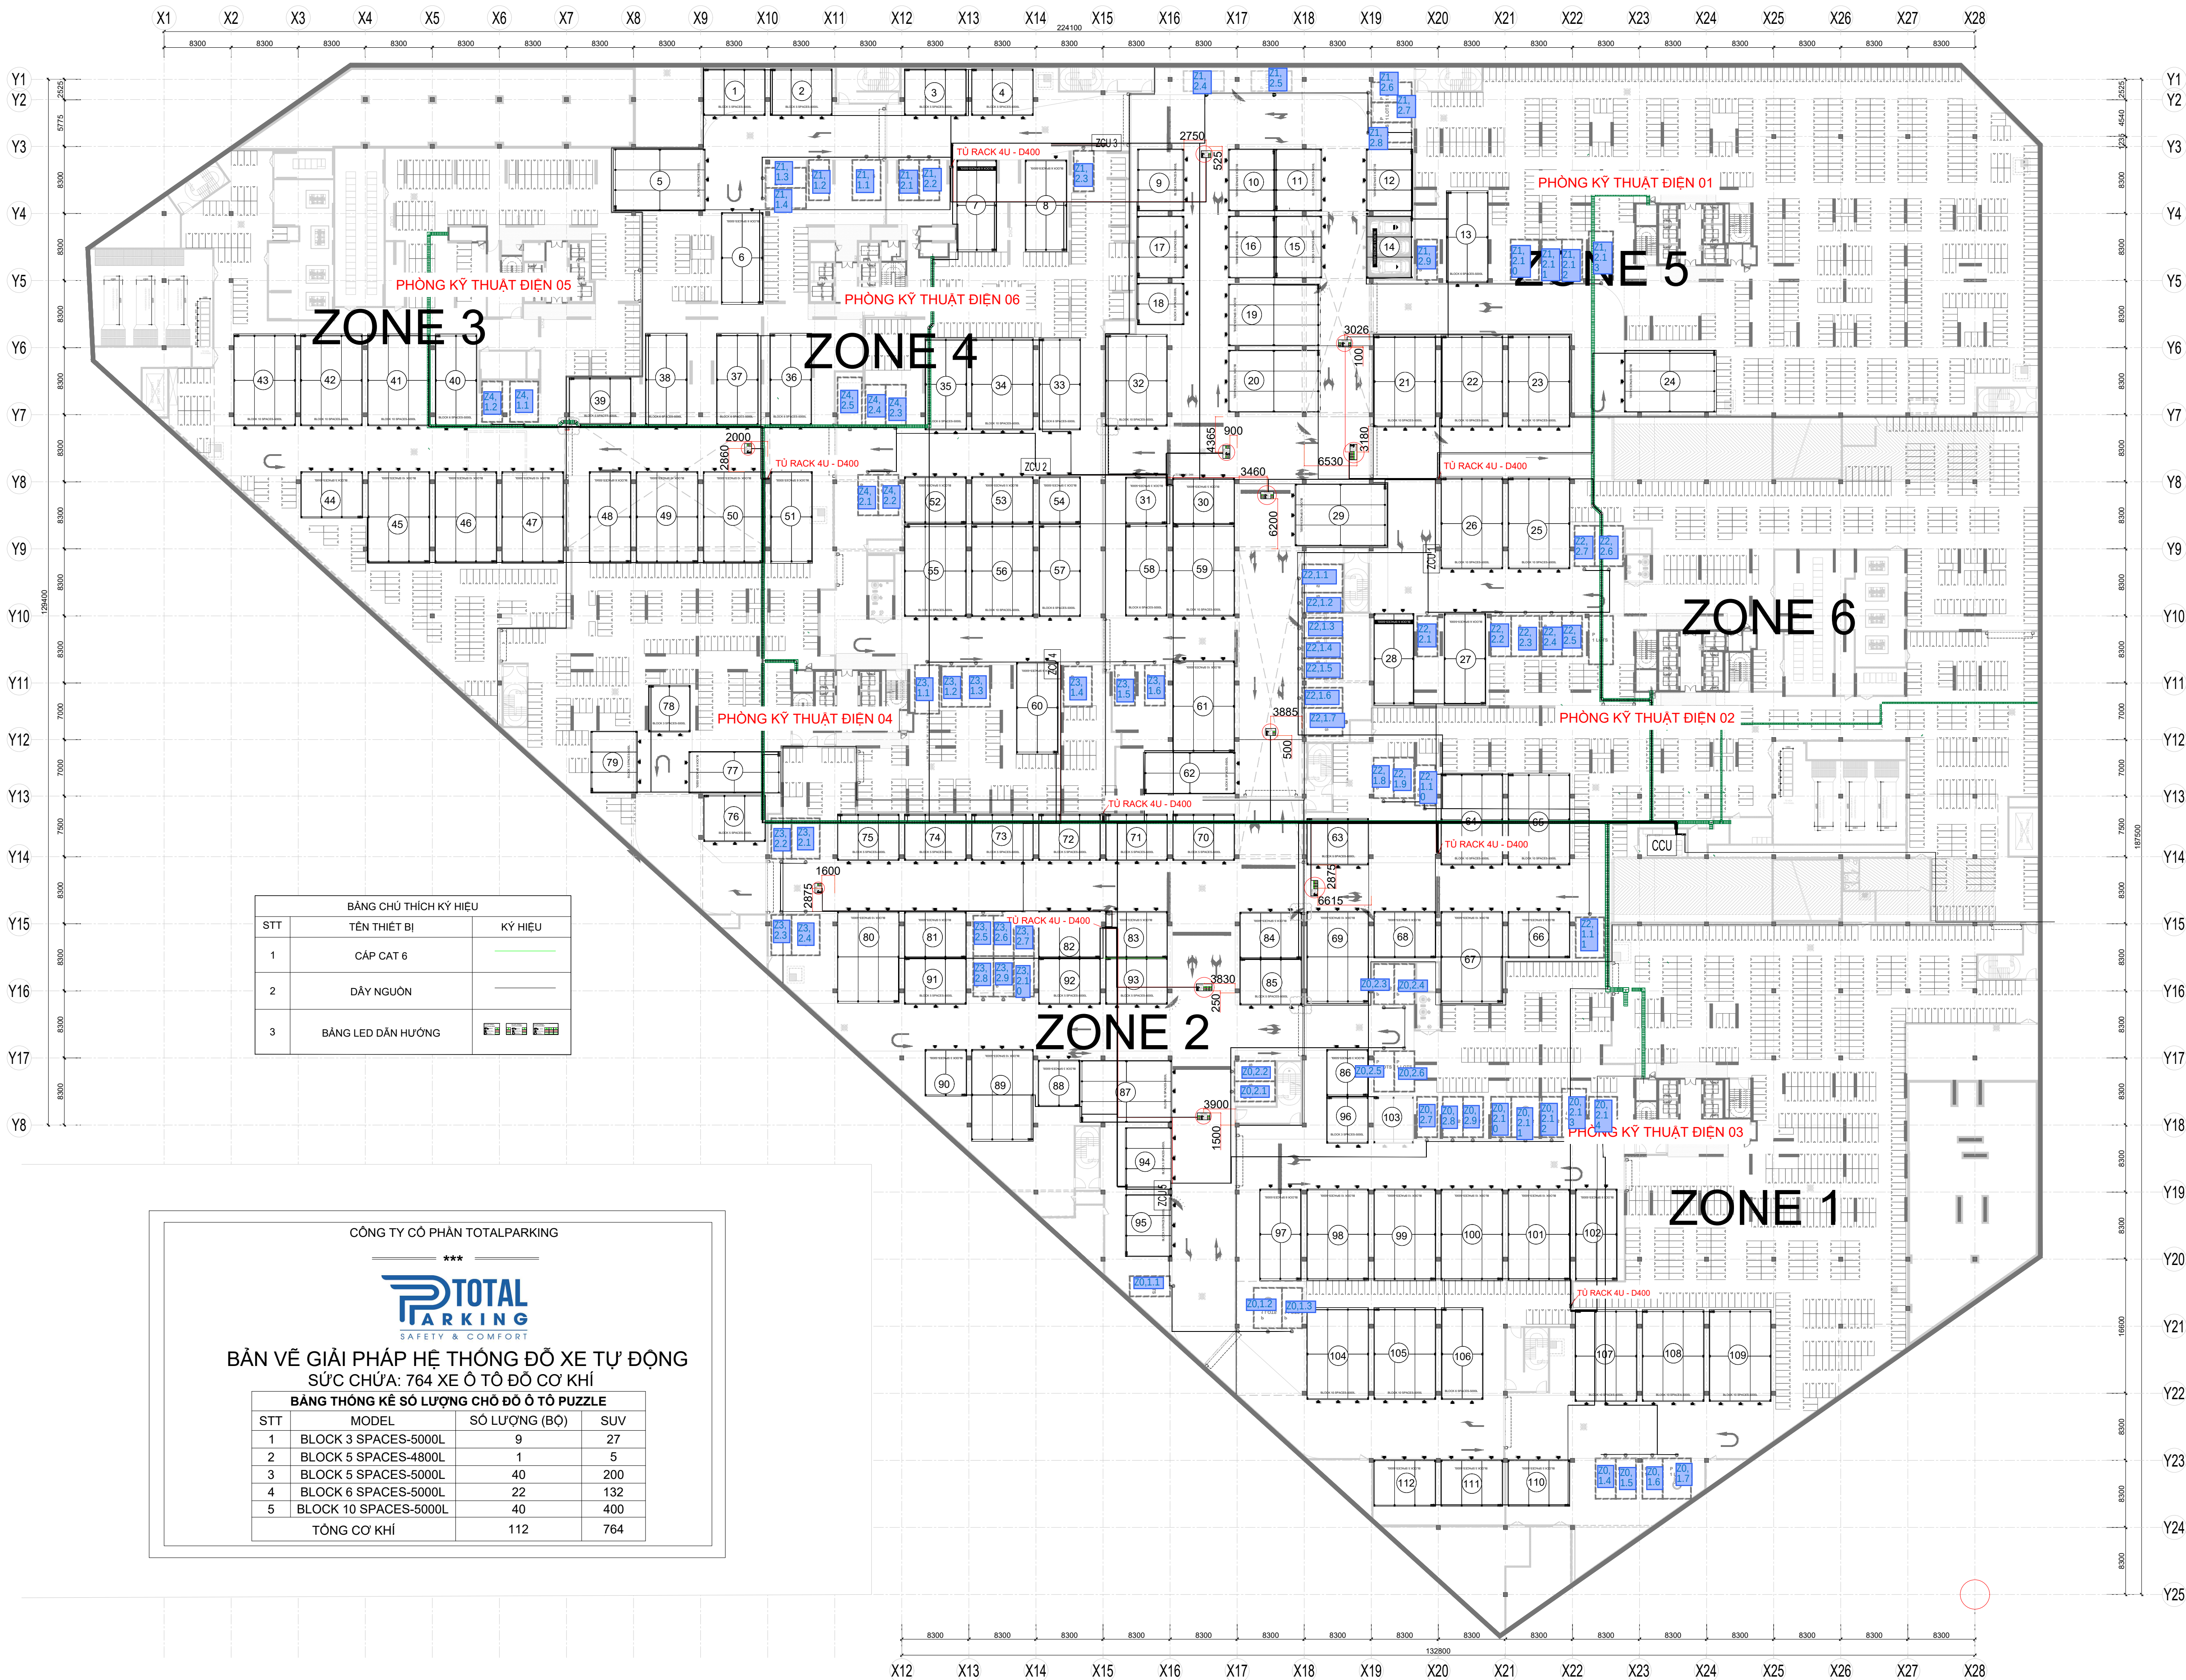

BẢNG CHỦ THÍCH KÝ HIỆU		
STT	TÊN THIẾT BỊ	KÝ HIỆU
1	CÁP CAT 6	
2	DÂY NGUỒN	
3	BẢNG LED DẪN HƯỚNG	

CÔNG TY CỔ PHẦN TOTALPARKING

TOTAL

PARKING

SAFETY & COMFORT

BẢN VẼ GIẢI PHÁP HỆ THỐNG ĐỖ XE TỰ ĐỘNG

SỨC CHỨA: 764 XE Ô TÔ ĐỖ CƠ KHÍ

BẢNG THÔNG KÊ SỐ LƯỢNG CHỖ ĐỖ Ô TÔ PUZZLE

STT	MODEL	SỐ LƯỢNG (BỘ)	SUV
1	BLOCK 3 SPACES-5000L	9	27
2	BLOCK 5 SPACES-4800L	1	5
3	BLOCK 5 SPACES-5000L	40	200
4	BLOCK 6 SPACES-5000L	22	132
5	BLOCK 10 SPACES-5000L	40	400
TỔNG CƠ KHÍ		112	764

MẶT BẰNG TỔNG THỂ DÂY TÍN HIỆU TẦNG HẦM - CLUSTER 01

PROJECT NAME - TÊN DỰ ÁN:
THE CONSTRUCTION AT LOTS C3-CH01, C3-CH02, C3-CH03, C3-CX01 AND C3-CX02 WITHIN THE NEW URBAN AREA PROJECT OF TÂY MÔ - ĐÀI MỎ (LUMI HÀ NỘI)

CÔNG TRÌNH TẠI LÔ ĐẤT C3-CH01, C3-CH02, C3-CH03, C3-CX01 VÀ C3-CX02 THUỘC DỰ ÁN KHU ĐÔ THỊ MỚI TÂY MÔ - ĐÀI MỎ (LUMI HÀ NỘI)

VENUE - ĐỊA ĐIỂM:
LOT C3-CH01-1, TÂY MÔ - ĐÀI MỎ NEW URBAN AREA PROJECT - VINHOMES PARK, TÂY MÔ WARD, HÀ NỘI CITY.
Ô C3-CH01-1, DỰ ÁN KHU ĐÔ THỊ MỚI TÂY MÔ - ĐÀI MỎ, VINHOMES PARK, PHƯỜNG TÂY MÔ, THÀNH PHỐ HÀ NỘI.

INVESTOR - CHỦ ĐẦU TƯ:
ANH SAO COMMERCIAL DEVELOPMENT AND TRADING LIMITED LIABILITY COMPANY
CÔNG TY TNHH THƯƠNG MẠI VÀ PHÁT TRIỂN KINH DOANH ÁNH SAO

ADDRESS - ĐỊA CHỈ:
LOT C3-CH01-1, TÂY MÔ - ĐÀI MỎ NEW URBAN AREA PROJECT - VINHOMES PARK, TÂY MÔ WARD, HÀ NỘI CITY.
Ô C3-CH01-1, DỰ ÁN KHU ĐÔ THỊ MỚI TÂY MÔ - ĐÀI MỎ, VINHOMES PARK, PHƯỜNG TÂY MÔ, THÀNH PHỐ HÀ NỘI.

TEL: 088480715 FAX: 088465274

Examined with no objection .

Examined, observation added Resubmission not required.

Examined and Resubmission required.

Signature:

Name:

Date:

DESIGN CONSULTANT-TƯ VẤN THIẾT KẾ:
CÔNG TY CỔ PHẦN INNO
inno
CREATIVITY AT WORK
INNO.JSC COMPANY
ADDRESS: NO. 87 YÊN HÒA, YÊN HÒA, CẦU GIẤY, HÀ NỘI
ĐỊA CHỈ: SỐ 87 YÊN HÒA, PH. YÊN HÒA, CẦU GIẤY, HÀ NỘI
TEL: 0243 212 1776 FAX: 0243 212 1776

Examined with no objection .

Examined, observation added Resubmission not required.

Examined and Resubmission required.

Approved by:

Name:

Date:

Checked by:

Name:

Date:

MAIN CONTRACTOR- NHÀ THẦU THI CÔNG
NEWTECONS INVESTMENT
CONSTRUCTION JOINT STOCK COMPANY
CÔNG TY CỔ PHẦN ĐẦU TƯ XÂY DỰNG NEWTECONS
NEWTECONS GROUP
ADDRESS - ĐỊA CHỈ:
NEWTECONS TOWER - 96 PHAN DANG LUU STREET, DUC NHUAN WARD, HO CHI MINH
NEWTECONS TOWER, 96 PHAN DANG LUU, PHƯỜNG ĐỨC NHUAN, THÀNH PHỐ HỒ CHÍ MINH

Approved by:

Name: LƯU VINH KIET

Date:

CONTRACTOR- NHÀ THẦU THI CÔNG
CÔNG TY CỔ PHẦN TOTAL PARKING
TOTAL PARKING
JOINT STOCK COMPANY
TOTAL PARKING
SAFETY & COMFORT
ADDRESS - ĐỊA CHỈ:
TÒA NHÀ HAVEE, LÔ D2, KHU ĐÁU GIÁ QSD
PHƯỜNG HÀ ĐÔNG, TP. HÀ NỘI
LOT D2, LAND USE RIGHT AUTON, HÀ ĐÔNG WARD, HÀ NỘI CITY
TEL: (84) (024) 33 11 7744 / FAX: (84) (024) 33 11 7748

Approved by:

Name: PHẠM MINH CHIẾN

Date:

Drawing by:

Name: LÊ TRUNG VINH

Date:

PACKAGE: GỒI THẦU:

MECHANICAL CAR PARKING SYSTEM

DRAWING TYPE - LOẠI BẢN VẼ:
☐ Method Statement (MOS) ☒ Shop Drawing (SD)

DRAWING NAME - TÊN BẢN VẼ:
MẶT BẰNG TỔNG THỂ DÂY TÍN HIỆU TẦNG HẦM - CLUSTER 01

SUBMIT NO - MÃ BẢN VẼ: LM-CL1-BAS-NTCP-SHD-0003-01.1

REV - PHIÊN BẢN: 01

SCALE - TỈ LỆ: As indicated

DATE - NGÀY:

DWG NO - SỐ BẢN VẼ: