


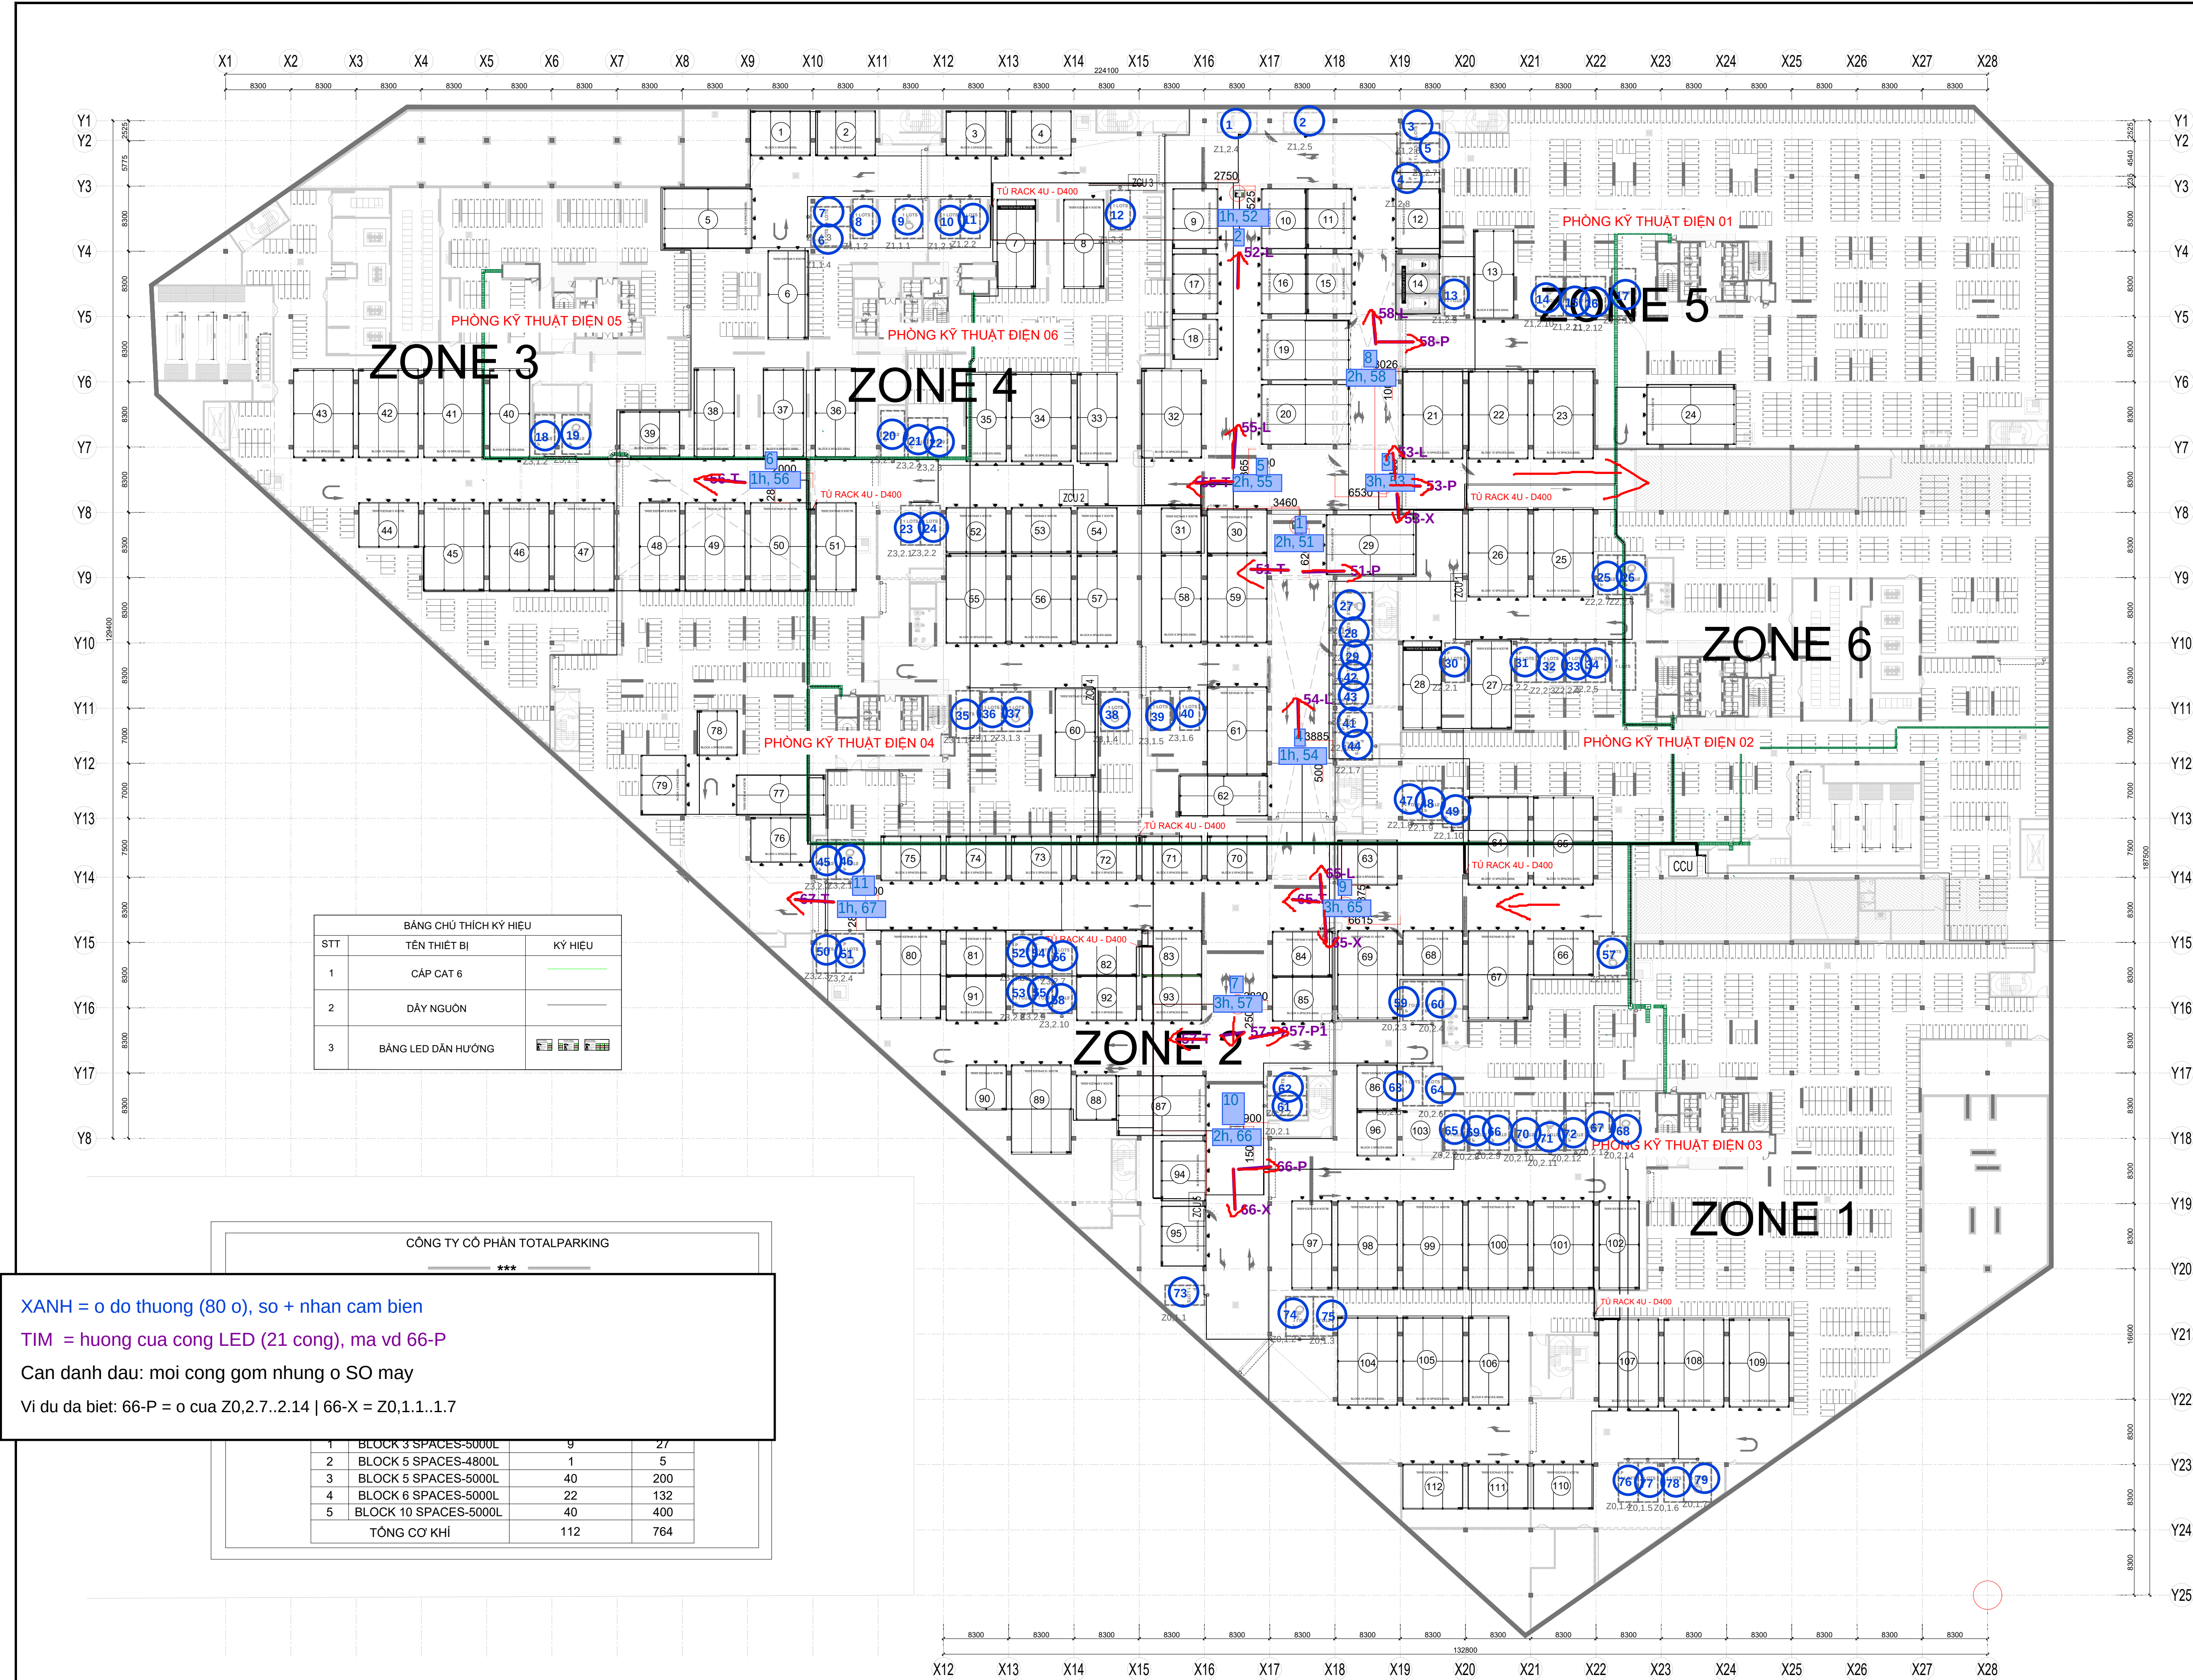

MẶT BẰNG TỔNG THỂ DÂY TÍN HIỆU TẦNG HẦM - CLUSTER 01

PROJECT NAME - TÊN DỰ ÁN:
THE CONSTRUCTION AT LOTS C3-CH01, C3-CH02, C3-CH03, C3-CX01 AND C3-CX02 WITHIN THE NEW URBAN AREA PROJECT OF TÂY MÔ - ĐẠI MÔ (LUMI HÀ NỘI)

CÔNG TRÌNH TẠI LÔ ĐẤT C3-CH01, C3-CH02, C3-CH03, C3-CX01 VÀ C3-CX02 THUỘC DỰ ÁN KHU ĐÔ THỊ MỚI TÂY MÔ - ĐẠI MÔ (LUMI HÀ NỘI)

VENUE - ĐỊA ĐIỂM:
LOT C3-CH01-1, TÂY MÔ - ĐẠI MÔ NEW URBAN AREA PROJECT - VINHOMES PARK, TÂY MÔ WARD, HÀ NỘI CITY.
Ô C3-CH01-1, DỰ ÁN KHU ĐÔ THỊ MỚI TÂY MÔ - ĐẠI MÔ, VINHOMES PARK, PHƯỜNG TÂY MÔ, THÀNH PHỐ HÀ NỘI.

INVESTOR - CHỦ ĐẦU TƯ:
ANH SAO COMMERCIAL DEVELOPMENT AND TRADING LIMITED LIABILITY COMPANY
CÔNG TY TNHH THƯƠNG MẠI VÀ PHÁT TRIỂN KINH DOANH ÁNH SAO

ADDRESS - ĐỊA CHỈ:
LOT C3-CH01-1, TÂY MÔ - ĐẠI MÔ NEW URBAN AREA PROJECT - VINHOMES PARK, TÂY MÔ WARD, HÀ NỘI CITY.
Ô C3-CH01-1, DỰ ÁN KHU ĐÔ THỊ MỚI TÂY MÔ - ĐẠI MÔ, VINHOMES PARK, PHƯỜNG TÂY MÔ, THÀNH PHỐ HÀ NỘI.

TEL: 088480715 FAX: 088465274

Examined with no objection .	Examined, observation added Resubmission not required.	Examined and Resubmission required.
☐	☐	☐

Signature:

Name: Date:

DESIGN CONSULTANT-TƯ VẤN THIẾT KẾ:
CÔNG TY CỔ PHẦN INNO
inno
CREATIVITY AT WORK
INNO JSC COMPANY
ADDRESS: NO. 87 YÊN HÒA, YÊN HÒA, CẦU GIẤY, HÀ NỘI
ĐỊA CHỈ: SỐ 87 YÊN HÒA, PH. YÊN HÒA, CẦU GIẤY, HÀ NỘI
TEL: 0243 212 1776 FAX: 0243 212 1776

Examined with no objection .	Examined, observation added Resubmission not required.	Examined and Resubmission required.
☐	☐	☐

Approved by:

Name: Date:

Checked by:

Name: Date:

MAIN CONTRACTOR- NHÀ THẦU THI CÔNG
NEWTECONS INVESTMENT
CONSTRUCTION JOINT STOCK COMPANY
CÔNG TY CỔ PHẦN ĐẦU TƯ XÂY DỰNG NEWTECONS

NEWTECONS GROUP

ADDRESS - ĐỊA CHỈ:
NEWTECONS TOWER - 96 PHAN DANG LUU STREET, DUC NHUAN WARD, HO CHI MINH
NEWTECONS TOWER, 96 PHAN DANG LUU, PHƯỜNG ĐỨC NHUAN, THÀNH PHỐ HỒ CHÍ MINH

Approved by:

Name: LƯU VINH KIET Date:

CONTRACTOR- NHÀ THẦU THI CÔNG
CÔNG TY CỔ PHẦN TOTAL PARKING
TOTAL PARKING
JOINT STOCK COMPANY
TOTAL PARKING
SAFETY & COMFORT

ADDRESS - ĐỊA CHỈ:
TÒA NHÀ HAVEE, LÔ D2, KHU ĐÁU GIÁ QSD
PHƯỜNG HÀ ĐÔNG, TP. HÀ NỘI
LOT D2, LAND USE RIGHT AUTON, HÀ ĐÔNG WARD, HÀ NỘI CITY
TEL: (84) (024) 33 11 7744 / FAX: (84) (024) 33 11 7748

Approved by:

Name: PHẠM MINH CHIẾN Date:

Drawing by:

Name: LÊ TRUNG VINH Date:

PACKAGE- GỒI THẦU:

MECHANICAL CAR PARKING SYSTEM

DRAWING TYPE - LOẠI BẢN VẼ:
☐ Method Statement (MOS) ☒ Shop Drawing (SD)

DRAWING NAME - TÊN BẢN VẼ:
MẶT BẰNG TỔNG THỂ DÂY TÍN HIỆU TẦNG HẦM - CLUSTER 01

SUBMIT NO - MÃ BẢN VẼ: LM-CL1-BAS-NTCP-SHD-0003-01.1

REV - PHIÊN BẢN: 01

SCALE - TỈ LỆ: As indicated

DATE - NGÀY:

DWG NO - SỐ BẢN VẼ: