


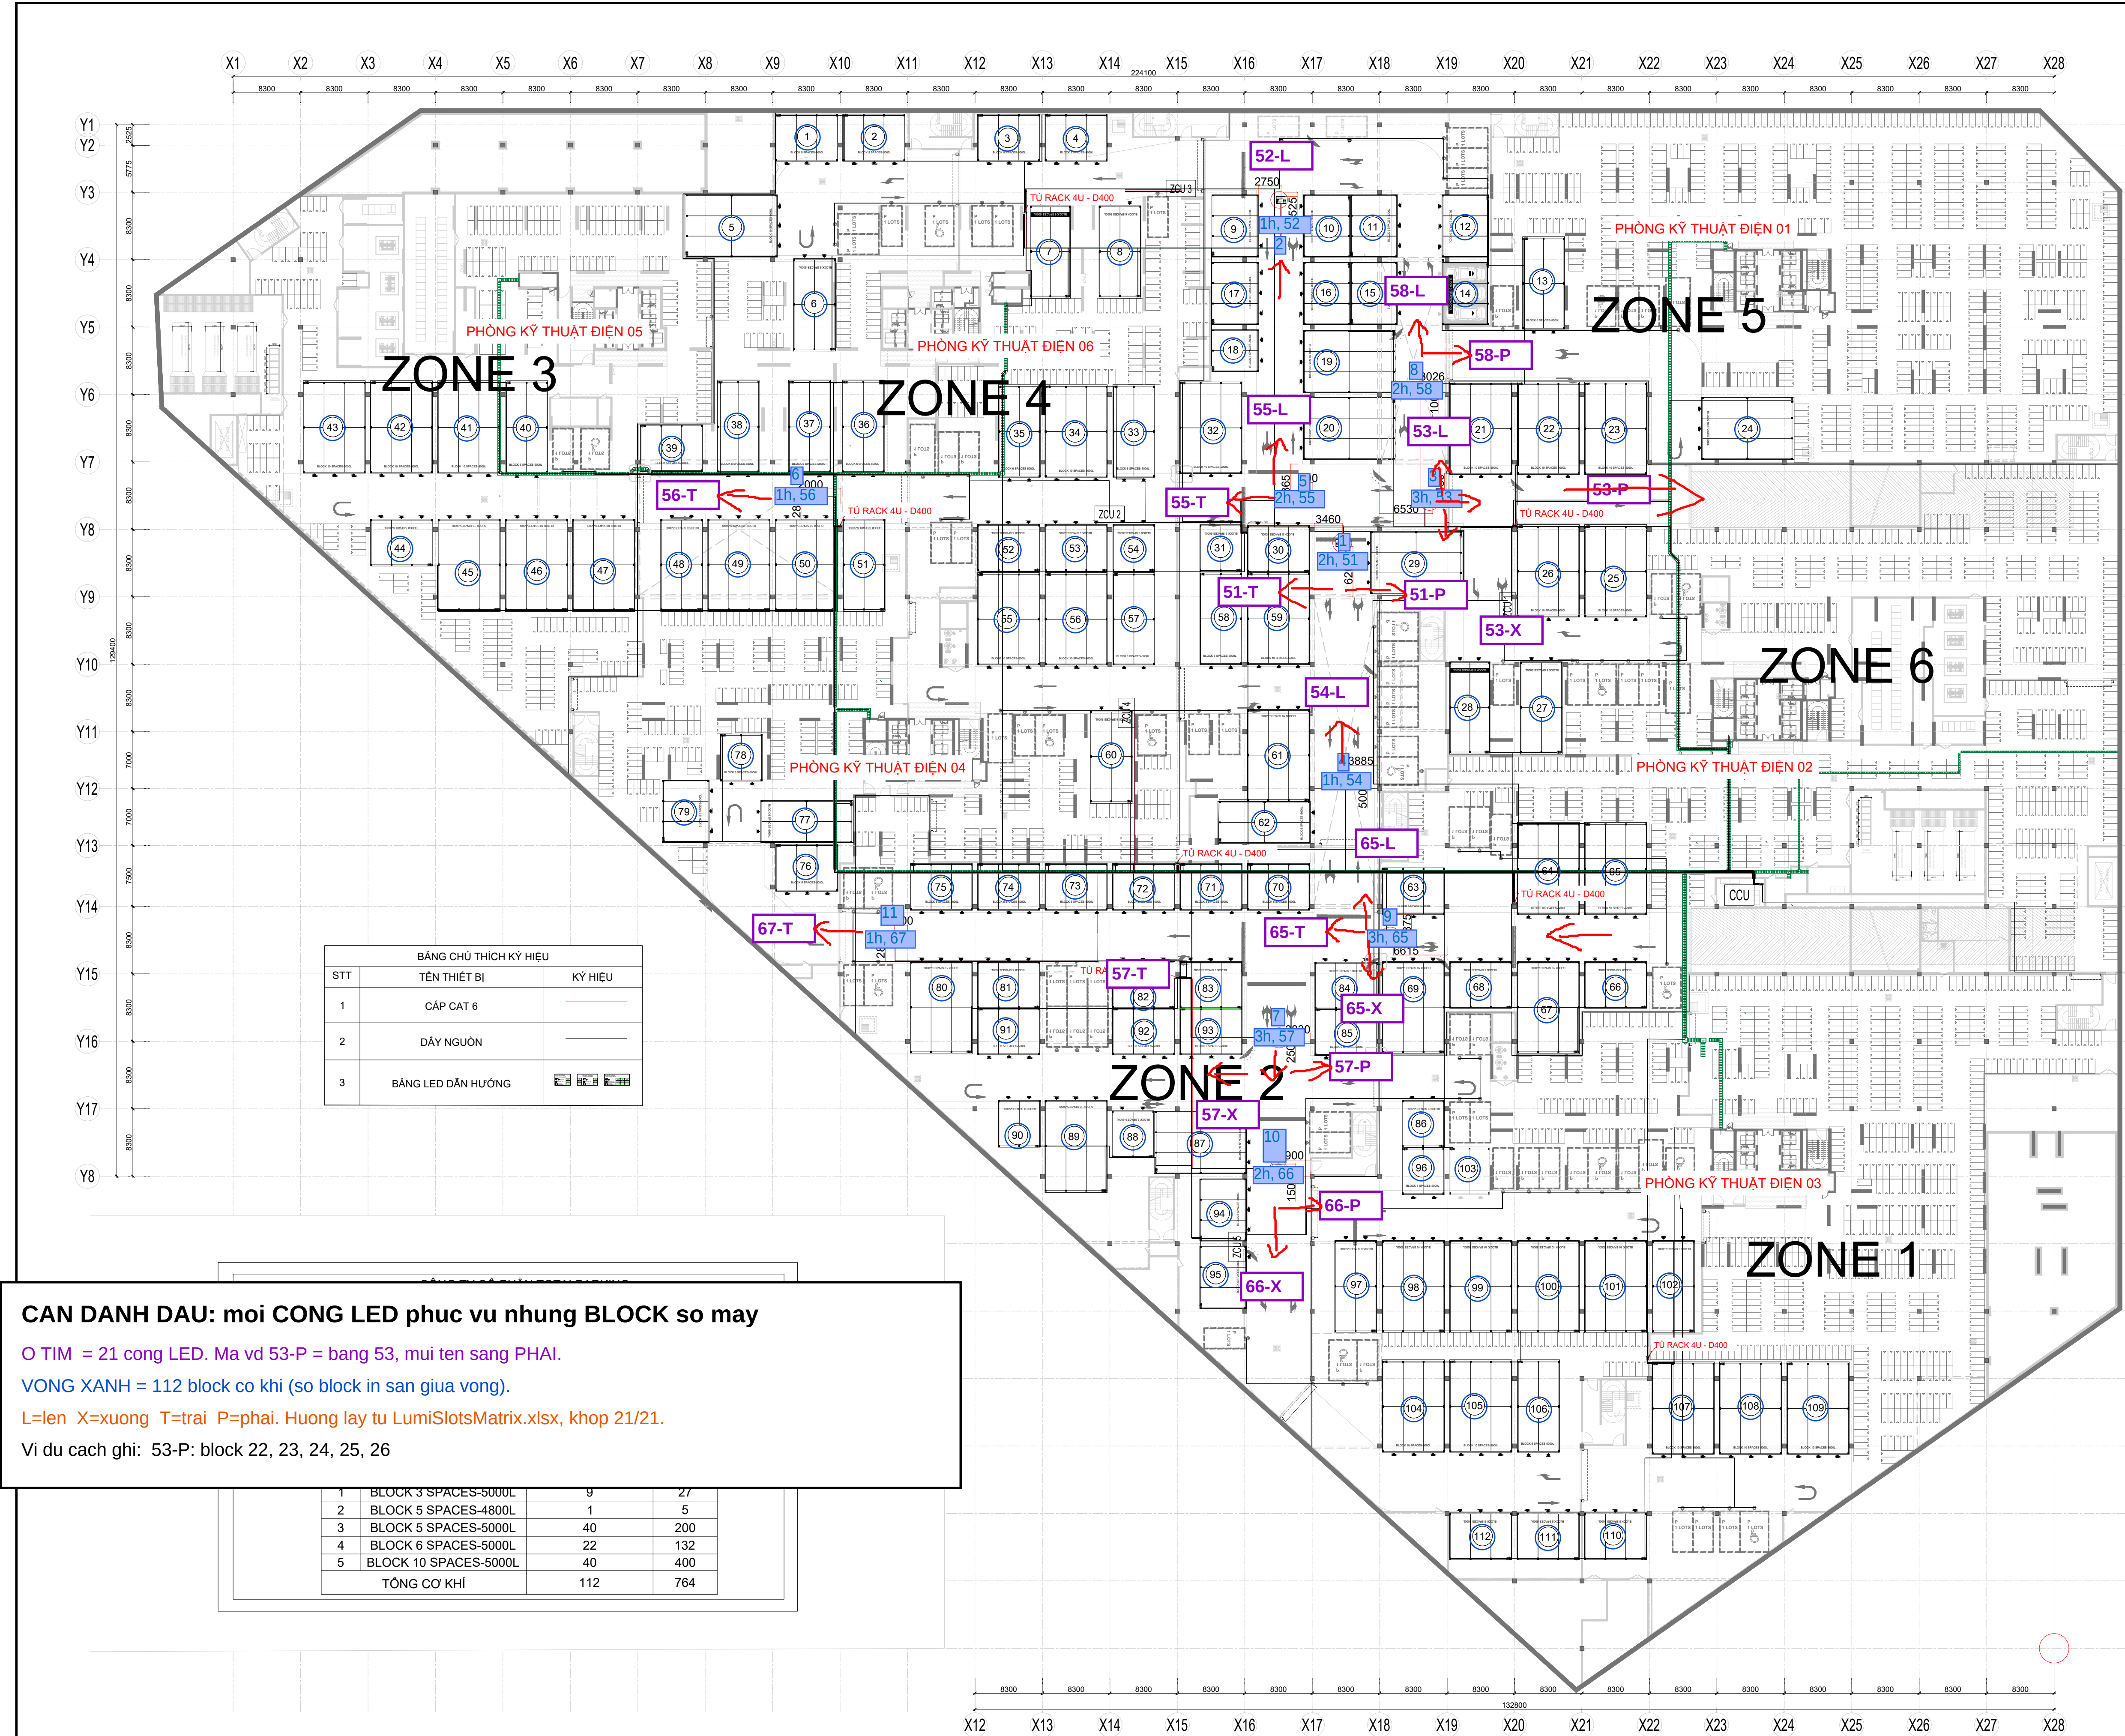

STT	TÊN THIẾT BỊ	KÝ HIỆU
1	CÁP CAT 6	—
2	DÂY NGUỒN	—
3	BẢNG LED DẪN HƯỚNG	—

CAN DANH DAU: mọi CONG LED phục vụ nhưng BLOCK số máy

O TIM = 21 cong LED. Ma vd 53-P = bang 53, mui ten sang PHAI.

VONG XANH = 112 block co khi (so block in san gữa vong).

L=len X=xuong T=trai P=phai. Huong lay tu LumiSlotsMatrix.xlsx, khop 21/21.

Vi du cach ghi: 53-P: block 22, 23, 24, 25, 26

1	BLOCK 3 SPACES-5000L	9	27
2	BLOCK 5 SPACES-4800L	1	5
3	BLOCK 5 SPACES-5000L	40	200
4	BLOCK 6 SPACES-5000L	22	132
5	BLOCK 10 SPACES-5000L	40	400
TỔNG CƠ KHÍ		112	764

MẶT BẰNG TỔNG THỂ DÂY TÍN HIỆU TẦNG HẦM - CLUSTER 01

PROJECT NAME - TÊN DỰ ÁN:
THE CONSTRUCTION AT LOTS C3-CH01, C3-CH02, C3-CH03, C3-CX01 AND C3-CX02 WITHIN THE NEW URBAN AREA PROJECT OF TAY MO - DAI MO (LUMI HANOI)

CÔNG TRÌNH TẠI LÔ ĐẤT C3-CH01, C3-CH02, C3-CH03, C3-CX01 VÀ C3-CX02 THUỘC DỰ ÁN KHU ĐÔ THỊ MỚI TAY MÔ - ĐÀI MÔ (LUMI HÀ NỘI)

VENUE - ĐỊA ĐIỂM:
LOT C3-CH01-1, TAY MO - DAI MO NEW URBAN AREA PROJECT - VINHOMES PARK, TAY MO WARD, HANOI CITY.
Ô C3-CH01-1, DỰ ÁN KHU ĐÔ THỊ MỚI TAY MÔ, ĐÀI MÔ, VINHOMES PARK, PHƯỜNG TÂY MÔ, THÀNH PHỐ HÀ NỘI.

INVESTOR - CHỦ ĐẦU TƯ:
ANH SAO COMMERCIAL DEVELOPMENT AND TRADING LIMITED LIABILITY COMPANY
CÔNG TY TNHH THƯƠNG MẠI VÀ PHÁT TRIỂN KINH DOANH ÁNH SAO

ADDRESS - ĐỊA CHỈ:
LOT C3-CH01-1, TAY MO - DAI MO NEW URBAN AREA PROJECT - VINHOMES PARK, TAY MO WARD, HANOI CITY.
Ô C3-CH01-1, DỰ ÁN KHU ĐÔ THỊ MỚI TAY MÔ, ĐÀI MÔ, VINHOMES PARK, PHƯỜNG TÂY MÔ, THÀNH PHỐ HÀ NỘI.

TEL: 088480715 FAX: 088465274

Examined with no objection .
☐

Examined, observation added Resubmission not required.
☐

Examined and Resubmission required.
☐

Signature: _____

Name: _____ Date: _____

DESIGN CONSULTANT-TƯ VẤN THIẾT KẾ:
CÔNG TY CỔ PHẦN INNO
inno
CREATIVITY AT WORK
INNO JSC COMPANY
ADDRESS: NO. 87 YEN HUA, YEN HUA, CAU GIAY, HANOI
ĐỊA CHỈ: SỐ 87 YÊN HÒA, PH. YÊN HÒA, CẦU GIẤY, HÀ NỘI
TEL: 0243 212 1776 FAX: 0243 212 1776

Examined with no objection .
☐

Examined, observation added Resubmission not required.
☐

Examined and Resubmission required.
☐

Approved by: _____

Name: _____ Date: _____

Checked by: _____

Name: _____ Date: _____

MAIN CONTRACTOR-NHÀ THẦU THI CÔNG
NEWTECONS INVESTMENT
CONSTRUCTION JOINT STOCK COMPANY
CÔNG TY CỔ PHẦN ĐẦU TƯ XÂY DỰNG NEWTECONS
NEWTECONS GROUP

ADDRESS - ĐỊA CHỈ:
NEWTECONS TOWER - 96 PHAN DANG LUU STREET, DUC NHUAN WARD, HO CHI MINH
NEWTECONS TOWER, 96 PHAN DANG LUU, PHƯỜNG ĐỨC NHUAN, THÀNH PHỐ HỒ CHÍ MINH

Approved by: _____

Name: LƯU VINH KIET Date: _____

CONTRACTOR-NHÀ THẦU THI CÔNG
CÔNG TY CỔ PHẦN TOTAL PARKING
TOTAL PARKING
JOINT STOCK COMPANY
TOTAL PARKING
SAFETY & COMFORT

ADDRESS - ĐỊA CHỈ:
TÒA NHÀ HAVEE, LÔ D2, KHU ĐÁU GIÁ QSD
PHƯỜNG HÀ ĐÔNG, TP. HÀ NỘI
LOT D2, LAND USE RIGHT AUTON, HA DONG WARD, HA NOI CITY
TEL: (84) (024) 33 11 7744 / FAX: (84) (024) 33 11 7748

Approved by: _____

Name: PHẠM MINH CHIẾN Date: _____

Drawing by: _____

Name: LÊ TRUNG VINH Date: _____

PACKAGE: GỒI THẦU:

MECHANICAL CAR PARKING SYSTEM

DRAWING TYPE - LOẠI BẢN VẼ:
☐ Method Statement (MOS) ☒ Shop Drawing (SD)

DRAWING NAME - TÊN BẢN VẼ:
MẶT BẰNG TỔNG THỂ DÂY TÍN HIỆU TẦNG HẦM - CLUSTER 01

SUBMIT NO - MÃ BẢN VẼ: LM-CL1-BAS-NTCP-SHD-0003-01.1

REV - PHIÊN BẢN: 01

SCALE - TỈ LỆ: As indicated

DATE - NGÀY: _____

DWG NO - SỐ BẢN VẼ: _____

BANG DIEN - moi cong LED phuc vu nhung block nao

Cot 'zone dang khai' liet ke cac zone bang do dang khai trong he thong, de doi chieu - khong phai dap an.

Ma cong	Bang	Huong	Zone dang khai (ca bang)	Block phuc vu (dien vao day)
51-T	51	trai	zone 4	
51-P	51	phai	zone 4	
52-L	52	len	zone 5	
53-L	53	len	zone 4, 5, 6	
53-P	53	phai	zone 4, 5, 6	
53-X	53	xuong	zone 4, 5, 6	
54-L	54	len	zone 2	
55-T	55	trai	zone 4, 6	
55-L	55	len	zone 4, 6	
56-T	56	trai	zone 3	
57-T	57	trai	zone 1, 2	
57-P	57	phai	zone 1, 2	
57-X	57	xuong	zone 1, 2	
58-L	58	len	zone 5, 6	
58-P	58	phai	zone 5, 6	
65-L	65	len	zone 2, 6	
65-T	65	trai	zone 2, 6	
65-X	65	xuong	zone 2, 6	
66-P	66	phai	zone 1, 2	
66-X	66	xuong	zone 1, 2	
67-T	67	trai	zone 2	